
Schéma de brassage - GP4
ECOCERT

Dernière édition par Louis MEDO le 14/09/2026.

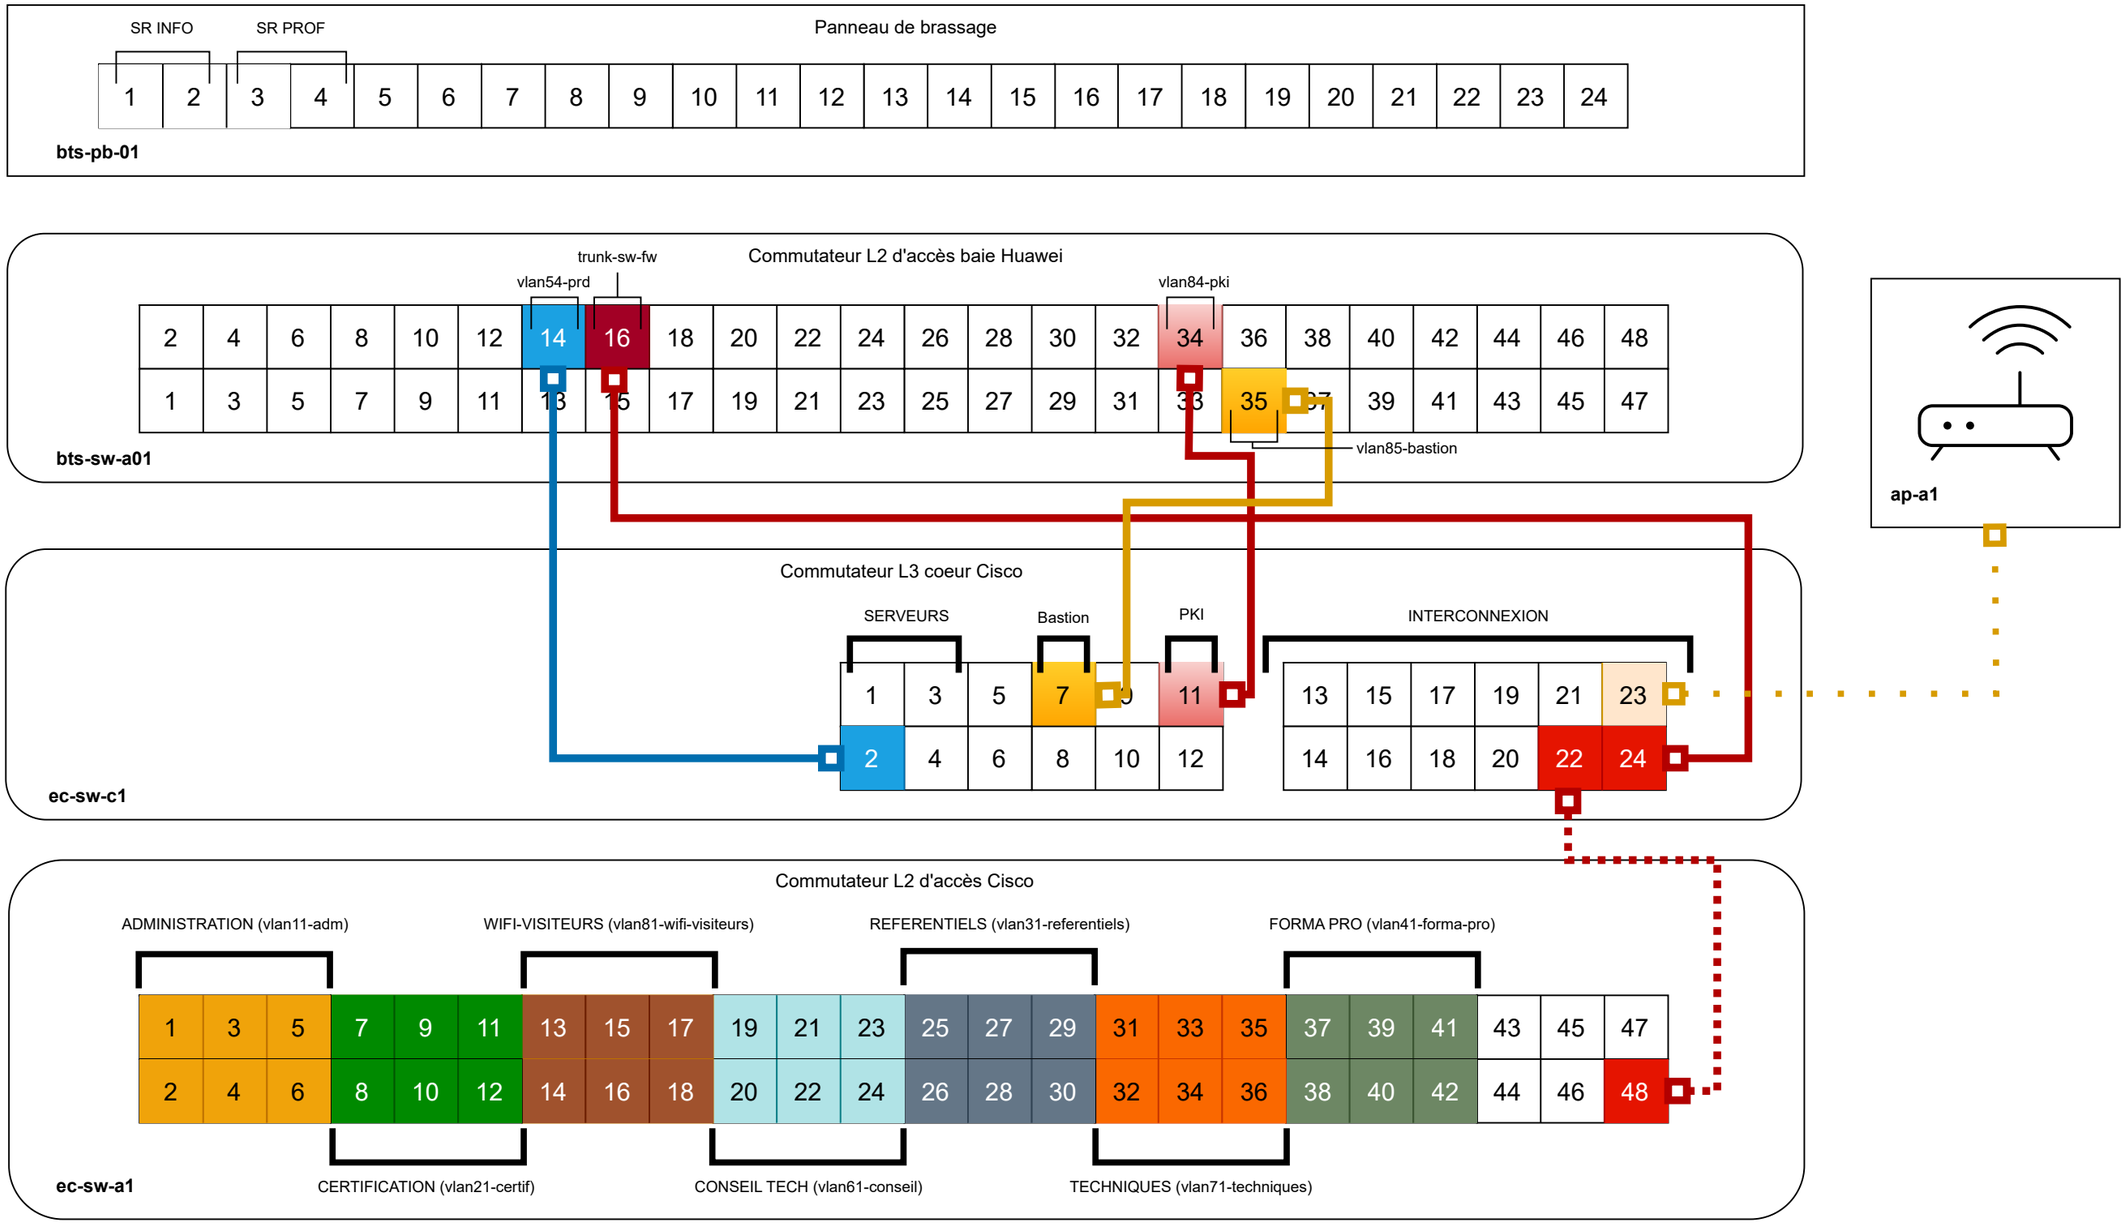

LÉGENDE

- VLAN 41 FORMA PRO
- VLAN 54 SERVEURS
- VLAN 61 CONSEIL TECH
- VLAN 84 PKI
- Liaison interconexion (sw/fw)
- VLAN 11 ADMINISTRATION
- VLAN 31 REFERENTIELS
- VLAN 85 Bastion
- VLAN 81 WIFI-VISITEURS
- VLAN 21 CERTIFICATION
- VLAN 71 TECHNIQUES
- Liaison avec tag (trunk)
- Liaison sans tag (access)
- Liaison trunk & native

ADRESSAGE

VLAN 11 ADMINISTRATION : 192.168.4.0/26 (de .1 à .62)
VLAN 21 CERTIFICATION : 192.168.4.64/27 (de .65 à .94)
VLAN 81 WIFI-VISITEURS : 192.168.4.96/27 (de .97 à .126)
VLAN 61 EXP TECHNIQUE : 192.168.4.128/27 (de .129 à .158)
VLAN 31 REFERENTIELS : 192.168.4.160/27 (de .161 à .190)
VLAN 41 FORMA PRO : 192.168.4.208/28 (de .209 à .222)
VLAN 54 Serveurs : 172.16.54.0 (de .1 à .124)
Liaison interconexion (sw/fw) : 192.168.14.248/29
VLAN 71 TECHNIQUES : 192.168.4.192/28 (de .193 à .206)
VLAN 84 PKI : 10.0.84.0/24 (de .1 à .254)
VLAN 85 Bastion : 10.0.85.0/24 (de .1 à .254)